
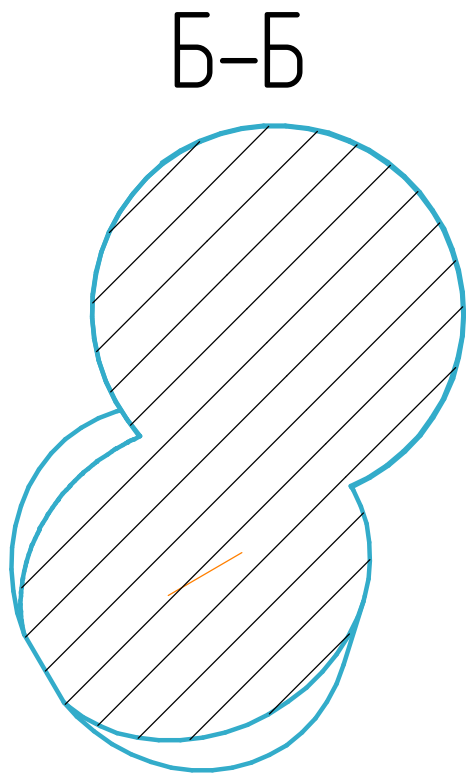
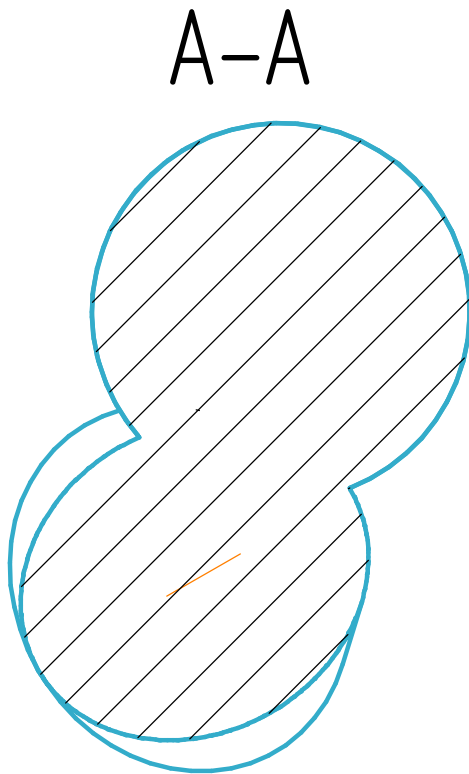


07.24944.01 СБ

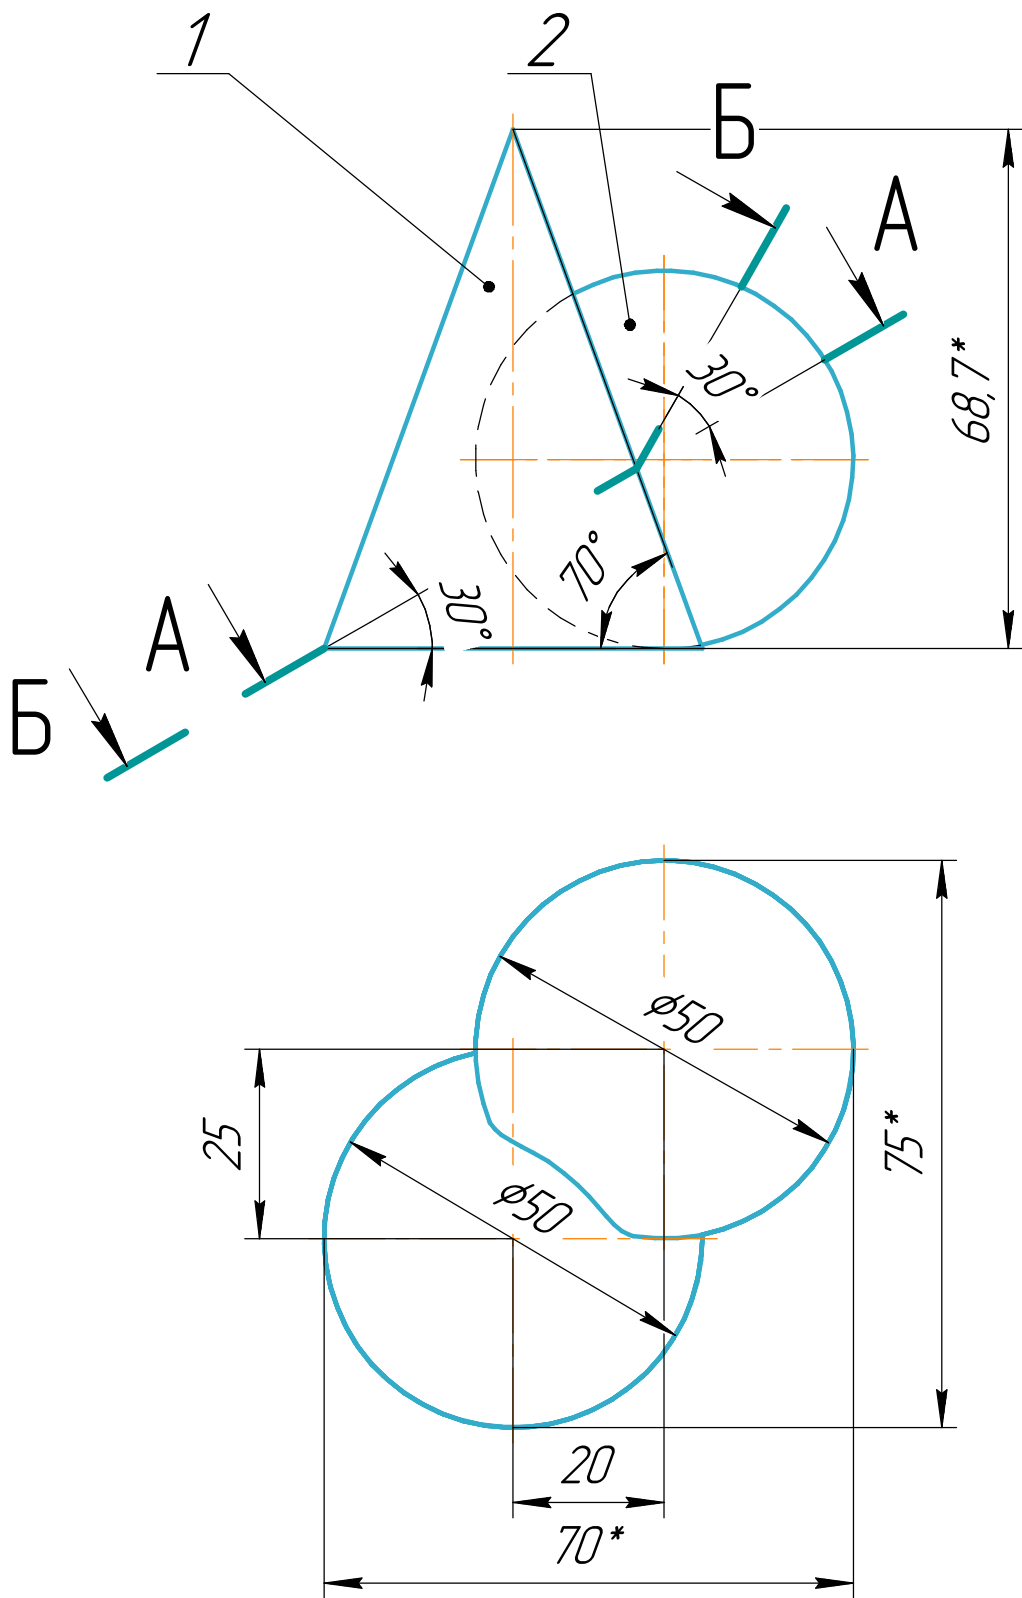

Формат	Зона	Поз.	Обозначение	Наименование	Кол.	Приме-чание
				Детали		
		1	07.24944.001	Конус	1	
		2	07.24944.002	Шар	1	
07.24944.01 СБ						
Изм.	Лист	№ докум.	Подп.	Дата	Лит.	Масса
Разраб.		Доронин		19.10		0,83
Пров.						1:1
Т.контр.					Лист 11	Листов 34
Н.контр.					НГУ - 2025	
Утв.						